
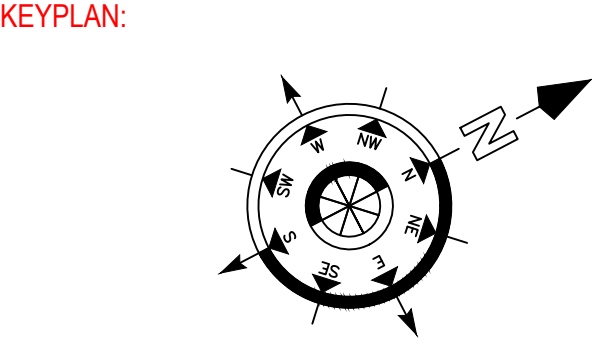


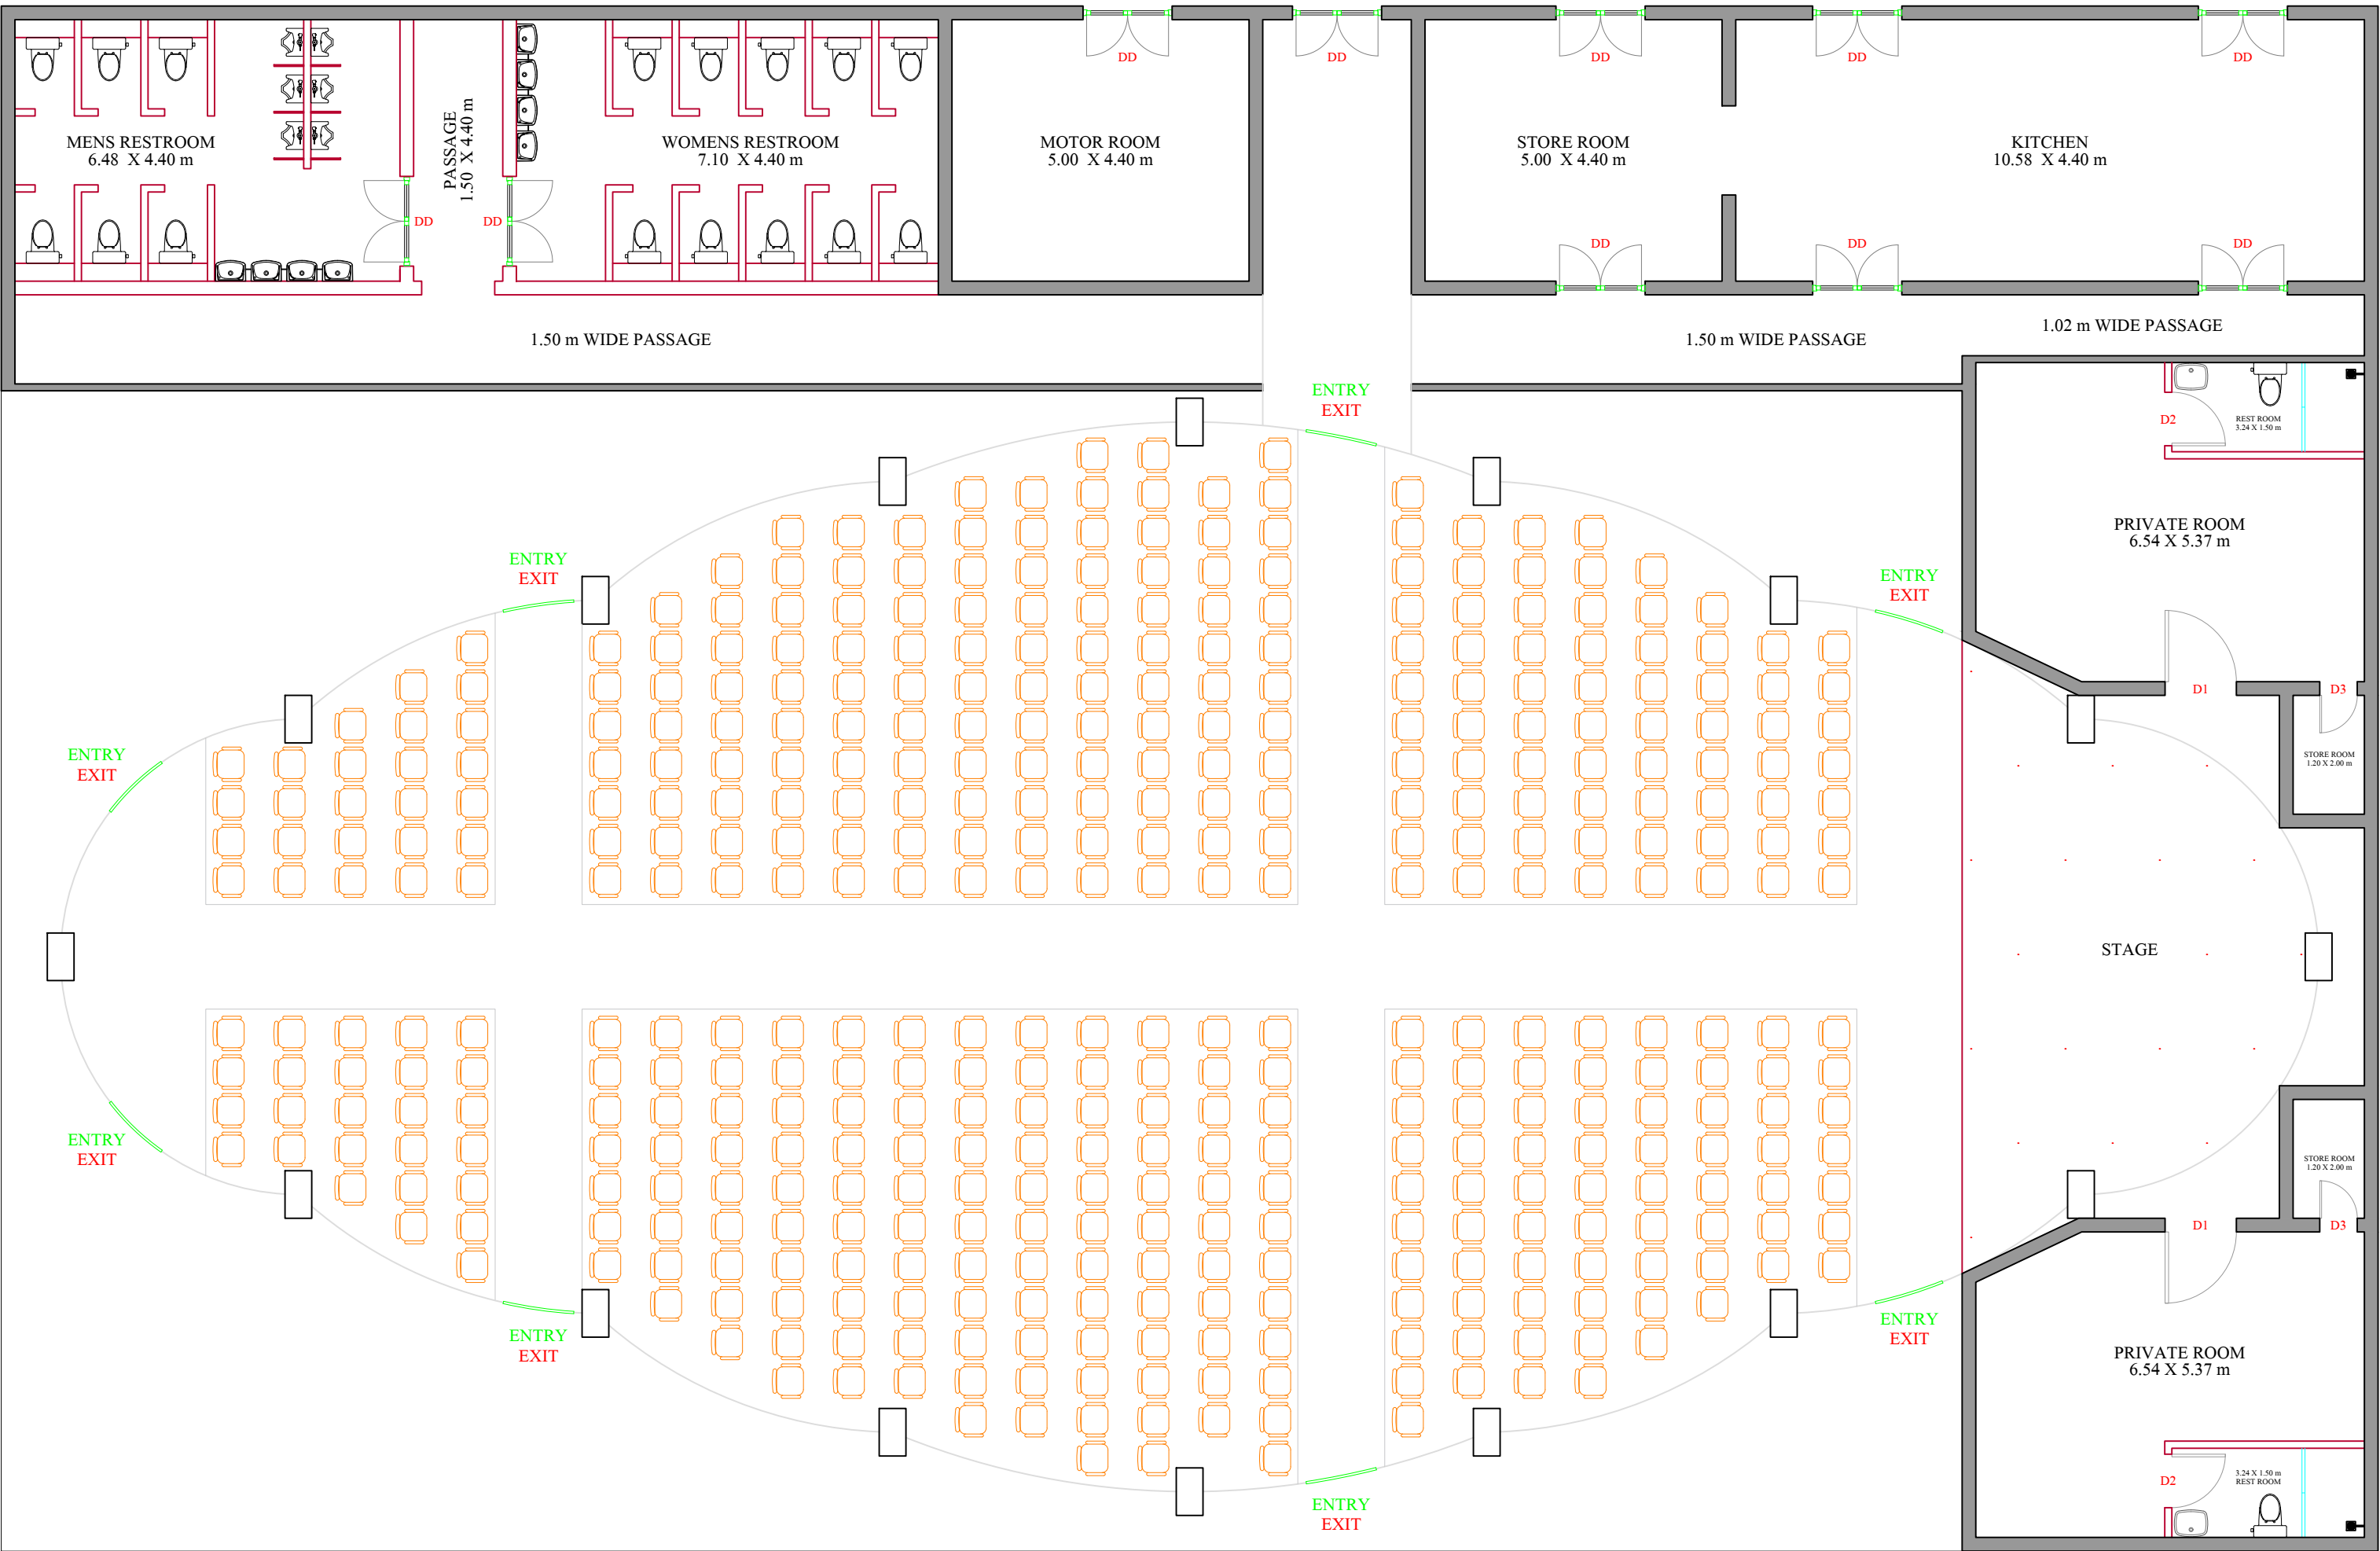

RESTROOM DETAILS:

| SPECIFICATION   | MENS                | WOMENS |
|-----------------|---------------------|--------|
| W/C COUNT       | 06 NOS              | 10 NOS |
| URINAL COUNT    | 06 NOS              | -      |
| WASH BASIN      | 04 NOS              | 04 NOS |
| AREA PER W/C    | 1.5 m <sup>2</sup>  |        |
| AREA PER URINAL | 0.46 m <sup>2</sup> | -      |

JOINERIES:

- DD - DOUBLE DOOR - 1.5m X 2.1m
- ENTRY \ EXIT - 1.2m X 2.1m
- D - GLAZED DOOR - 1.2m X 2.1m
- D1 - DOOR TYPE 1 - 1.2m X 2.1m
- D2 - DOOR TYPE 2 - 0.9m X 2.1m
- D3 - DOOR TYPE 3 - 0.6m X 2.1m

SEATING ARRANGEMENT:

- TOTAL SEATS 414
- AREA PER SEAT - 0.53m X 0.58m = 0.30 m<sup>2</sup>
- CLEAR DIST. BETWEEN ROWS = 0.50 m

AREA DETAILS:

ALL DIMENSIONS ARE IN METRE

TITLE:  
TENSILE\_STRUCTURE

CLIENT:  
CONVENTION\_HALL  
MUMBAI

|               |               |    |
|---------------|---------------|----|
| Drawn By :    | PARTHIBAN     |    |
| Checked By :  | VIMAL         |    |
| Approved By : | VK            |    |
| Scale:        | A2_1:100      |    |
| Date:         | 19/02/2026    | R2 |
| File:         | 2025/TEN/SAMP |    |

ARCHITECTS & DESIGNER:



TESCO STRUCTURES LLP  
New # 18/1,Old # 88/1, ARYA GOWDA ROAD,  
WEST MAMBALAM, CHENNAI - 33